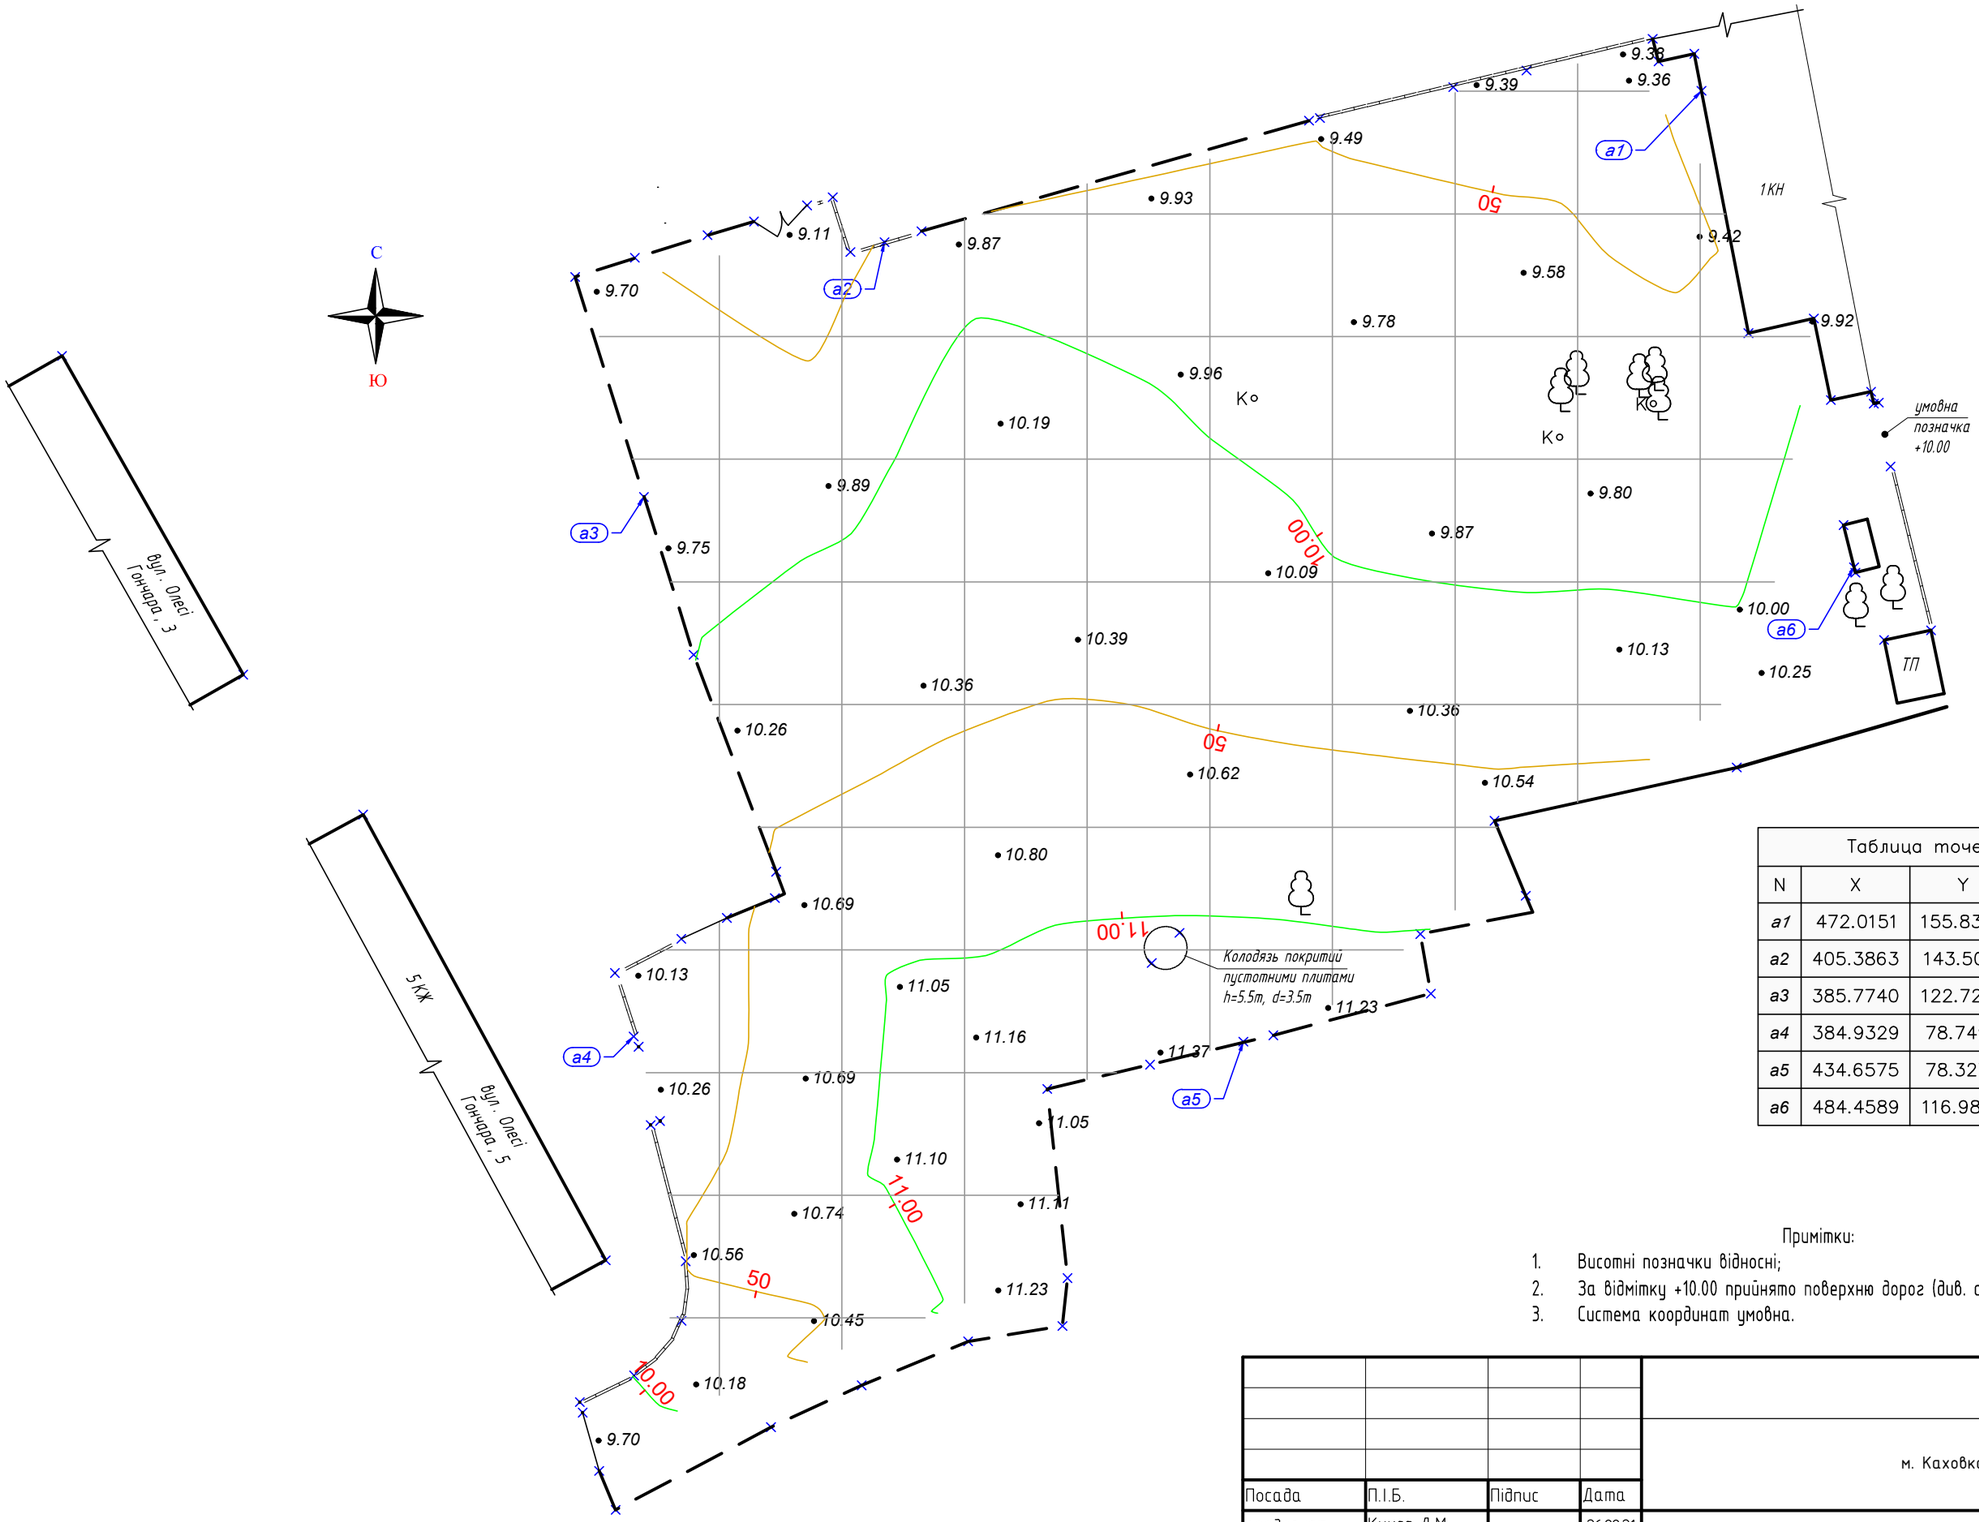

Таблица точек			
N	X	Y	Z
а1	472.0151	155.8372	11.72
а2	405.3863	143.5041	11.31
а3	385.7740	122.7266	11.85
а4	384.9329	78.7492	12.30
а5	434.6575	78.3273	13.47
а6	484.4589	116.9898	13.01

Примітки:

1. Висотні позначки відносні;
2. За відмітку +10.00 прийнято поверхню дорог (див. схему);
3. Система координат умовна.

Посада	П.І.Б.	Підпис	Дата
геодезист	Кукса Д.М.		26.08.21
виконроб	Желудкова В. А..		26.08.21

м. Каховка, Херсонська обл

Стадія	Аркуш	Аркушів

Планово-висотне знімання
М1:500

ТОВ «Олеся»
м. Нова Каховка

Копировал

Формат А3