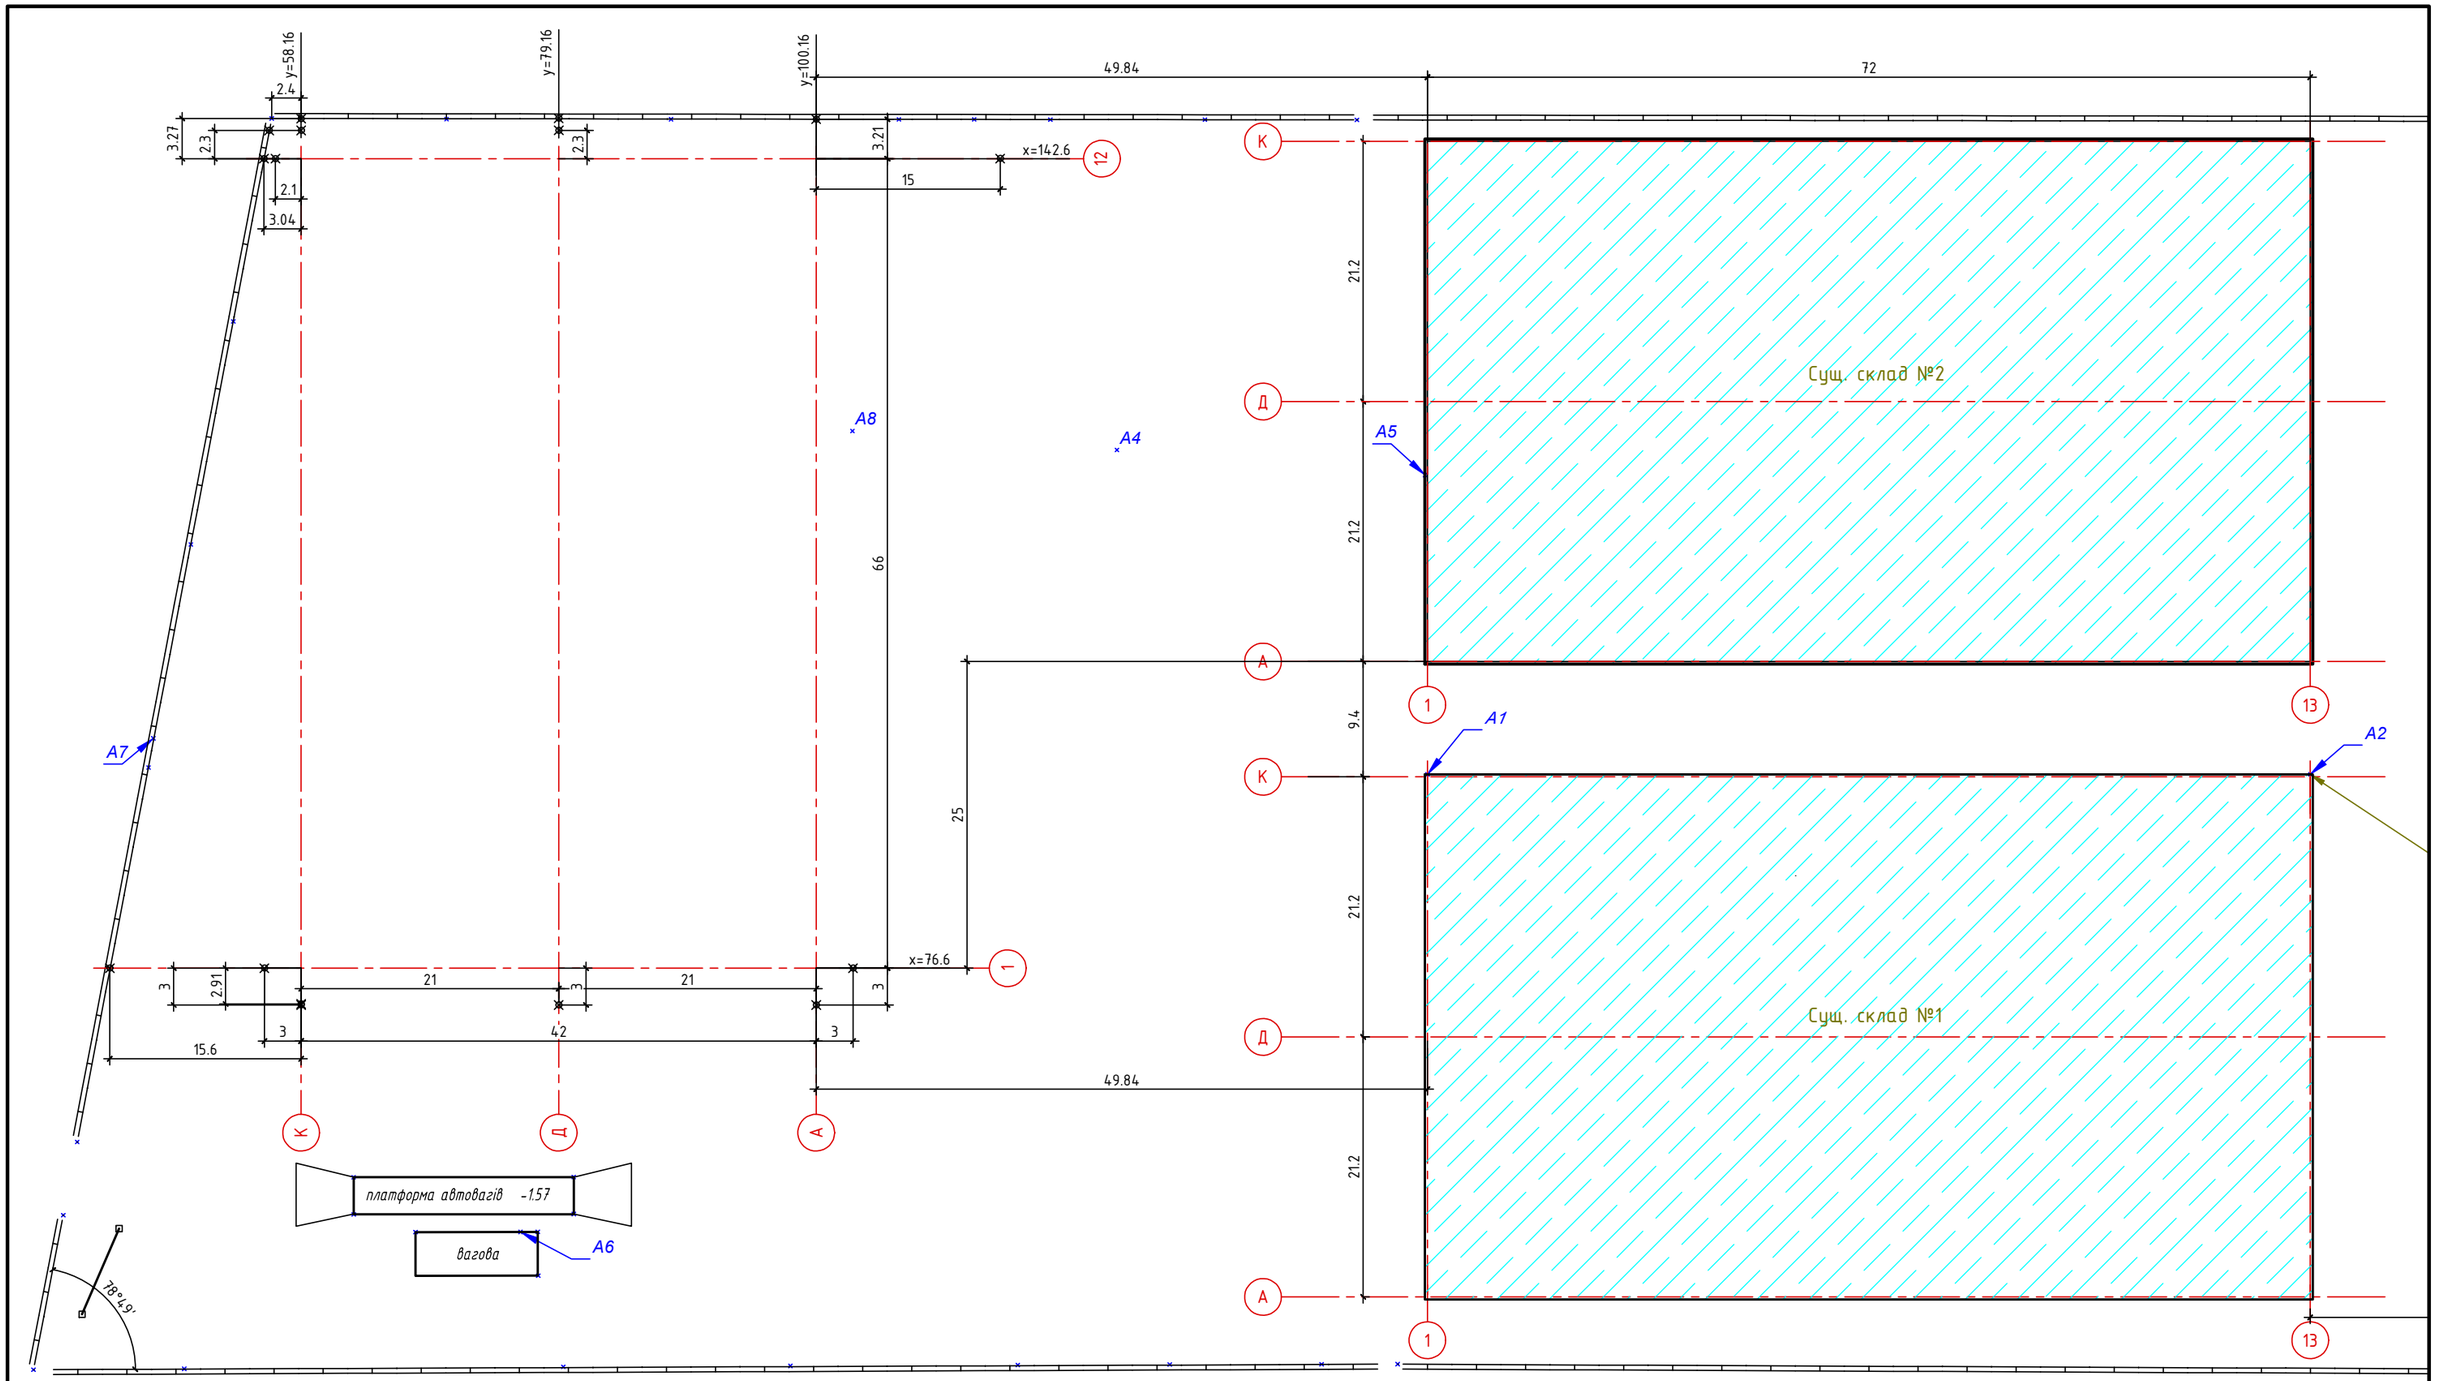

Таблица точек			
Имя	X	Y	H
a1	92.395	150.008	1.420
a2	92.405	222.001	1.424
a3	120.844	248.394	3.062
a4	118.849	124.691	0.956
a5	116.805	149.816	1.038
a6	55.101	76.051	−0.002
a7	95.341	46.106	−0.214
a8	120.392	103.115	0.574

Примітки:

1. Позначки відносні;
2. За відносну позначку 0.000 прийнята відносна позначка 0.000 складу №2.

Посада	П.І.Б.	Підпис	Дата
геодезист	Кукса Д.М.		19.08.21
виконроб	Желудкова В.А.		19.08.21

04-2021-АБ

м. Каховка, Херсонської області

Будівництво складу для напольного зберігання зерна

Стадія	Аркуш	Аркушів

Виконавча схема виносу осей зерноскладу М1:500

ТОВ «Олеся» м. Нова Каховка

Копировал

Формат А3