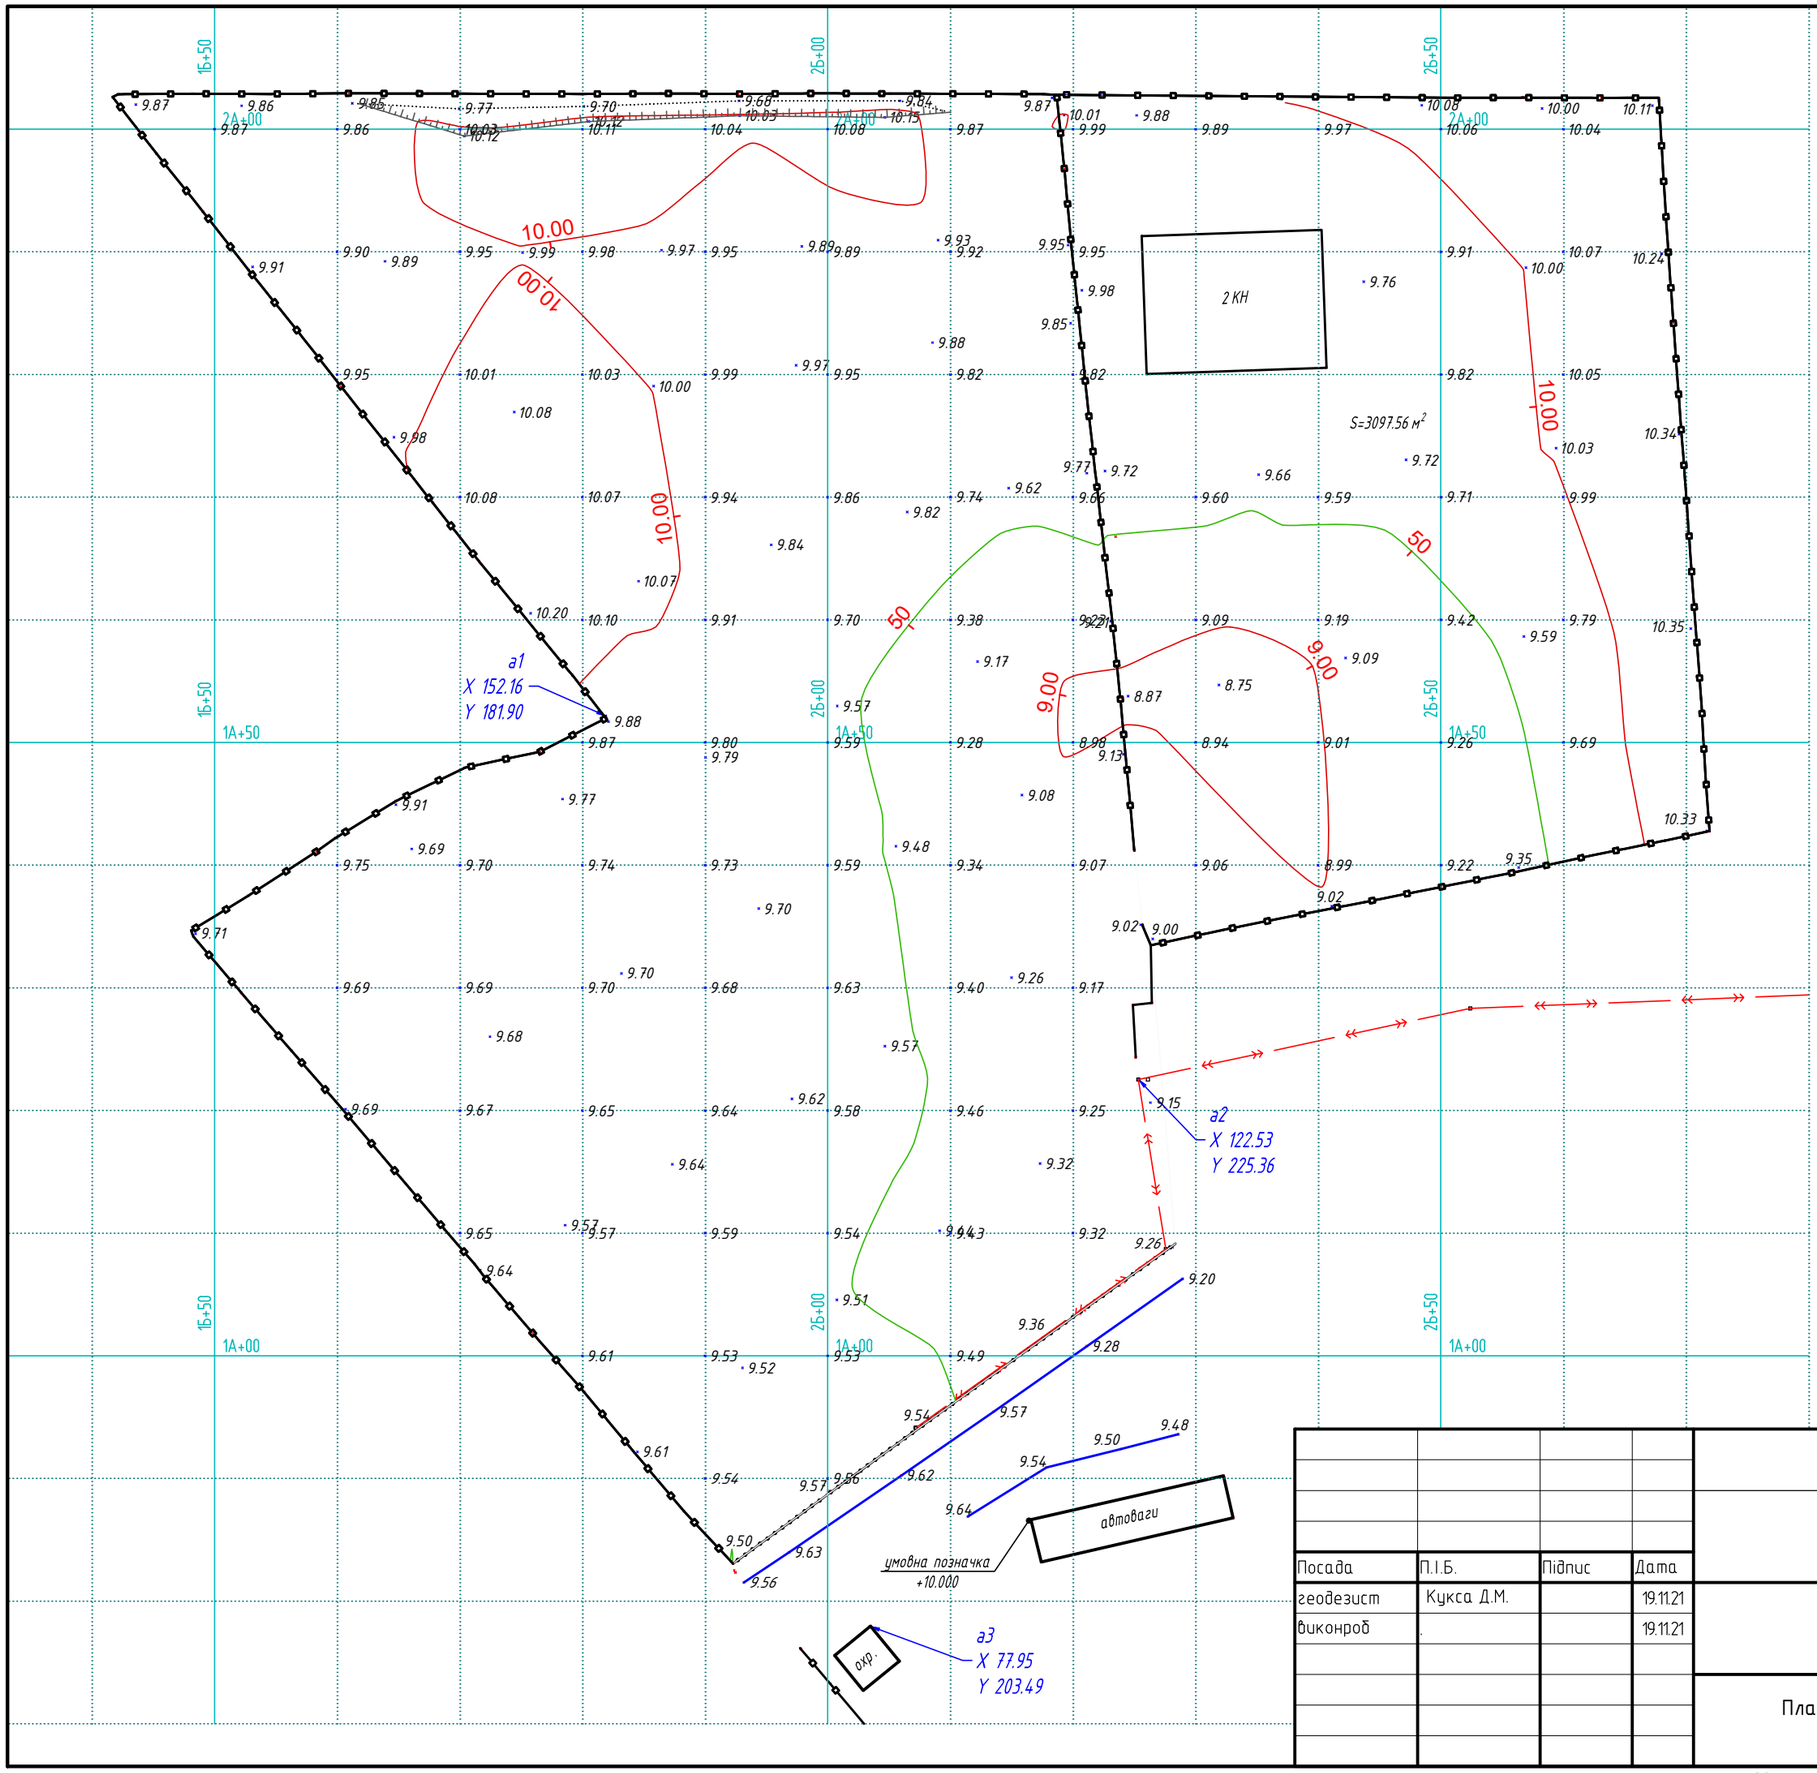


Примітки:

1. Висотні позначки відносні;
2. За позначку +10.00 прийнято верх пандусу біля автовагів;
3. Система координат умовна;
4. Координати базових точок:

| N | X | Y | Z |
|---|---|---|---|
| а1 | 152.165 | 181.897 | 11.921 |
| а2 | 122.527 | 225.359 | 11.016 |
| а3 | 77.951 | 203.491 | 12.206 |

| Посада | П.І.Б. | Підпис | Дата |
|---|---|---|---|
| геодезист | Кукса Д.М. | | 19.11.21 |
| виконроб | . | | 19.11.21 |

| Стадія | Аркуш | Аркушів |
|---|---|---|
| | | |

Планово-висотне знімання
М1:500

ТОВ «Олеся»
м. Нова Каховка

Копировал

Формат А3